简图

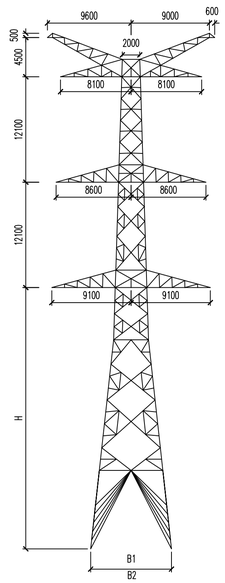

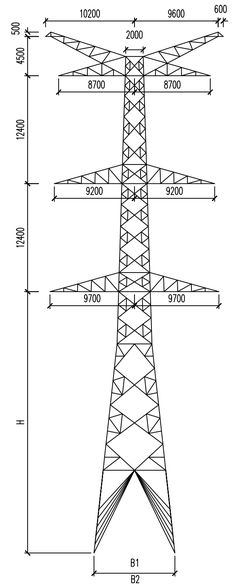

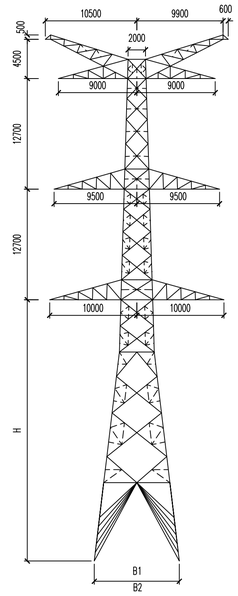

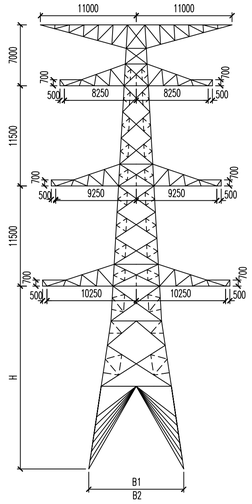

杆塔名称		5246-ZS1 型双回路直线塔								
呼称高 H(m)		36	39	42	45	48	51	54	57	60
全塔高 (m)		65.2	68.2	71.2	74.2	77.2	80.2	83.2	86.2	89.2
铁塔极开(mm)	正面B1	10600	11260	11920	12580	13240	13900	14560	15220	15880
	侧面B2	10600	11260	11920	12580	13240	13900	14560	15220	15880
材料指标(kg)		37912.7	39507.6	42677.8	44257.4	46391.5	50782.1	53393.5	55016.9	59394.4
使用数量(基)				4	1	5		1		
水平档距(m)		400								
垂直档距(m)		600								
备注		角钢塔								

杆塔名称		5246-ZS2 型双回路直线塔								
呼称高 H(m)		36	39	42	45	48	51	54	57	60
全塔高 (m)		65.8	68.8	71.8	74.8	77.8	80.8	83.8	86.8	89.8
铁塔极开(mm)	正面B1	10600	11260	11920	12580	13240	13900	14560	15220	15880
	侧面B2	10600	11260	11920	12580	13240	13900	14560	15220	15880
材料指标(kg)		44102.6	46140.8	49016.0	52381.0	55204.7	58388.1	60875.4	64273.9	67848.2
使用数量(基)				1	1		1	5	3	3
水平档距(m)		550								
垂直档距(m)		800								
备注		角钢塔								

杆塔名称		5246-ZS3 型双回路直线塔								
呼称高 H(m)		36	39	42	45	48	51	54	57	60
全塔高 (m)		66.4	69.4	72.4	75.4	78.4	81.4	84.4	87.4	90.4
铁塔极开(mm)	正面B1	11200	11920	12640	13360	14080	14800	15520	16240	16960
	侧面B2	11200	11920	12640	13360	14080	14800	15520	16240	16960
材料指标(kg)		48986.1	51374.8	53914.1	56395.6	58431.1	64007.2	66893.9	69658.3	72892.9
使用数量(基)				1	2	1	2	4		2
水平档距(m)		700								
垂直档距(m)		1100								
备注		角钢塔								

杆塔名称		5246-JS1 型双回路转角塔								
呼称高 H(m)		30	33	36	39	42	45	48	51	54
全塔高 (m)		60	63	66	69	72	75	78	81	84
铁塔极开(mm)	正面B1	13600	14500	15400	16300	17200	18100	19000	19900	20800
	侧面B2	13600	14500	15400	16300	17200	18100	19000	19900	20800
材料指标(kg)		77218.9	80327.8	85203.3	88409.7	93505.9	97909.9	102524.1	108153.7	111461.9
使用数量(基)						2		2		2
水平档距(m)		340/110								
垂直档距(m)		±600/±200								
备注		0~20°转角，角钢塔								

简图

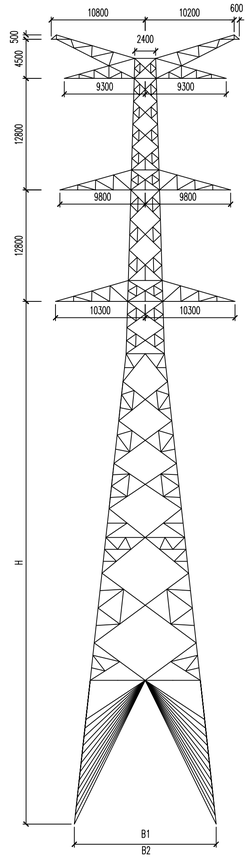

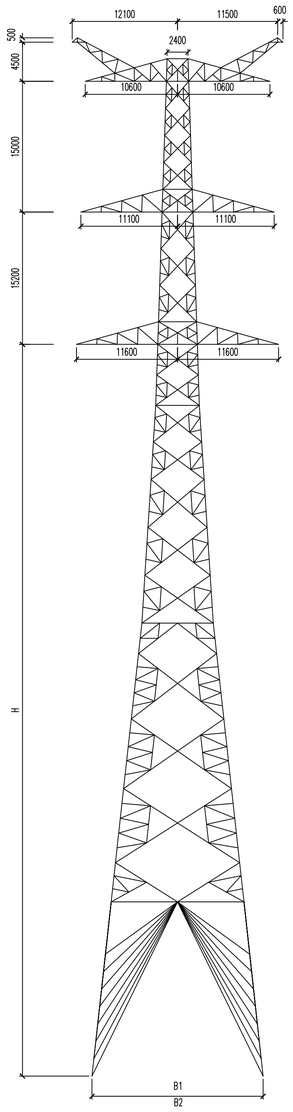

杆塔名称		5246-ZS4 型双回路直线塔			
呼称高 H(m)		60	66	72	78
全塔高 (m)		90.6	96.6	102.6	108.6
铁塔极开(mm)	正面B1	16280	17600	18920	20240
	侧面B2	16280	17600	18920	20240
材料指标(kg)		80091.1	87733.5	95009.3	104990.4
使用数量(基)		1	2	2	
水平档距(m)		650			
垂直档距(m)		1200			
备注		角钢塔			

杆塔名称		5246-ZS5 型双回路直线塔							
呼称高 H(m)		84	90	96	102	108	114	120	126
全塔高 (m)		119.2	125.2	131.2	137.2	143.2	149.2	155.2	161.2
铁塔极开(mm)	正面B1	19640	20960	22280	23600	24920	26240	27560	28880
	侧面B2	19640	20960	22280	23600	24920	26240	27560	28880
材料指标(kg)		130582.2	144343.8	164164.9	168711.8	187380.6	209526	214972.2	231662.1
使用数量(基)			2			1			
水平档距(m)		550							
垂直档距(m)		1200							
备注		角钢塔							

简图

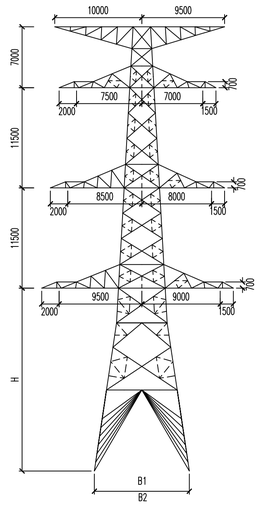

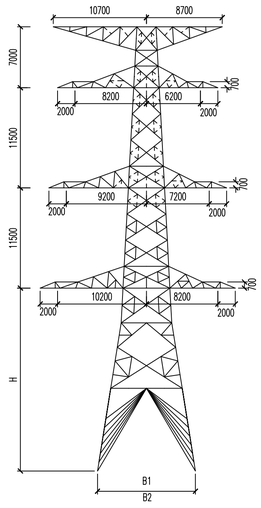

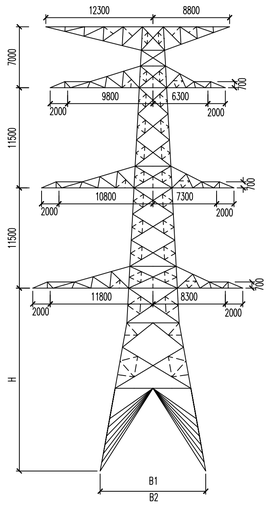

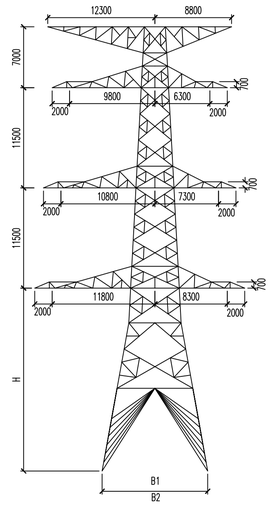

杆塔名称		5246-JS2 型双回路转角塔								
呼称高 H(m)		30	33	36	39	42	45	48	51	54
全塔高 (m)		60	63	66	69	72	75	78	81	84
铁塔极开(mm)	正面B1	13600	14500	15400	16300	17200	18100	19000	19900	20800
	侧面B2	13600	14500	15400	16300	17200	18100	19000	19900	20800
材料指标(kg)		77253.2	81395.8	85094	89568.6	94919.4	99796.8	104433	110838.7	116112.1
使用数量(基)							2	1		
水平档距(m)		340/110								
垂直档距(m)		±600/±200								
备注		20~40°转角，角钢塔								

杆塔名称		5246-JS3 型双回路转角塔								
呼称高 H(m)		30	33	36	39	42	45	48	51	54
全塔高 (m)		60	63	66	69	72	75	78	81	84
铁塔极开(mm)	正面B1	14120	15080	16040	17000	17960	18920	19880	20840	21800
	侧面B2	14120	15080	16040	17000	17960	18920	19880	20840	21800
材料指标(kg)		84655.2	88887.9	93354.4	97460.1	103552	108816.3	112889.8	120355.1	124117.7
使用数量(基)				1	1					
水平档距(m)		340/110								
垂直档距(m)		±600/±200								
备注		40~60°转角，角钢塔								

杆塔名称		5246-JS4 型双回路转角塔								
呼称高 H(m)		30	33	36	39	42	45	48	51	54
全塔高 (m)		60	63	66	69	72	75	78	81	84
铁塔极开(mm)	正面B1	15360	16440	17520	18600	19680	20760	21840	22920	24000
	侧面B2	15360	16440	17520	18600	19680	20760	21840	22920	24000
材料指标(kg)		93122.3	97963	104237.9	108655.9	113721.5	120955.4	126827.1	132415.3	138968.6
使用数量(基)						1		1		
水平档距(m)		340/110								
垂直档距(m)		±600/±200								
备注		60~80°转角，角钢塔								

杆塔名称		5246-JDG 型双回路转角塔								
呼称高 H(m)		27	30	33	36	39	42	45	48	51
全塔高 (m)		57	60	63	66	69	72	75	78	81
铁塔极开(mm)	正面B1	14280	15360	16440	17520	18600	19680	20760	21840	22920
	侧面B2	14280	15360	16440	17520	18600	19680	20760	21840	22920
材料指标(kg)		102315	109224.7	113951.7	120255.5	125676.2	130023.3	134174.6	143170.3	148412.9
使用数量(基)							2			
水平档距(m)		400/50								
垂直档距(m)		±1000/±50								
备注		80~90°转角兼终端，角钢塔								

广东省建设工程勘察设计出图专用章
单位名称:珠海电力设计院有限公司
业务范围:电力行业(送电工程,变电工程)专业甲级
资质证书编号:A244070284
有效期至:2023年12月31日

线路电气专业	签名	日期
		2023-07-21

珠海电力设计院有限公司

上寨至珠东北站双回线路开断接入碧山变500千伏线路	工程	施工图	设计阶段
批准		铁塔一览图(上寨侧)	
审核			
校核			
设计			
CAD制图			
比例			
2023年07月06日		图号	47-S50021S-A0101-11